AERODROME CHART - ICAO

ARP 36°39'48" N 051°27'53" E

AD ELEV -61FT

TWR 124.600, 121.700

NOSHAHR

RWY	Direction (TRUE)	THR	ELEV	Bearing Strength	GUND
10	108.64°	363959.59N 0512715.94E	−61FT	LCN55 Asphalt	−5FT
28	288.65°	363938.48N 0512833.58E	−71FT	LCN55 Asphalt	−5FT

TWY Width: 30 M, Asphalt, PCN: Info not available

DTHR RWY 10: 775 M.

DTHR RWY 28: 150 M.

DTHR RWY 28 COORD : 363940.03N 0512827.87E

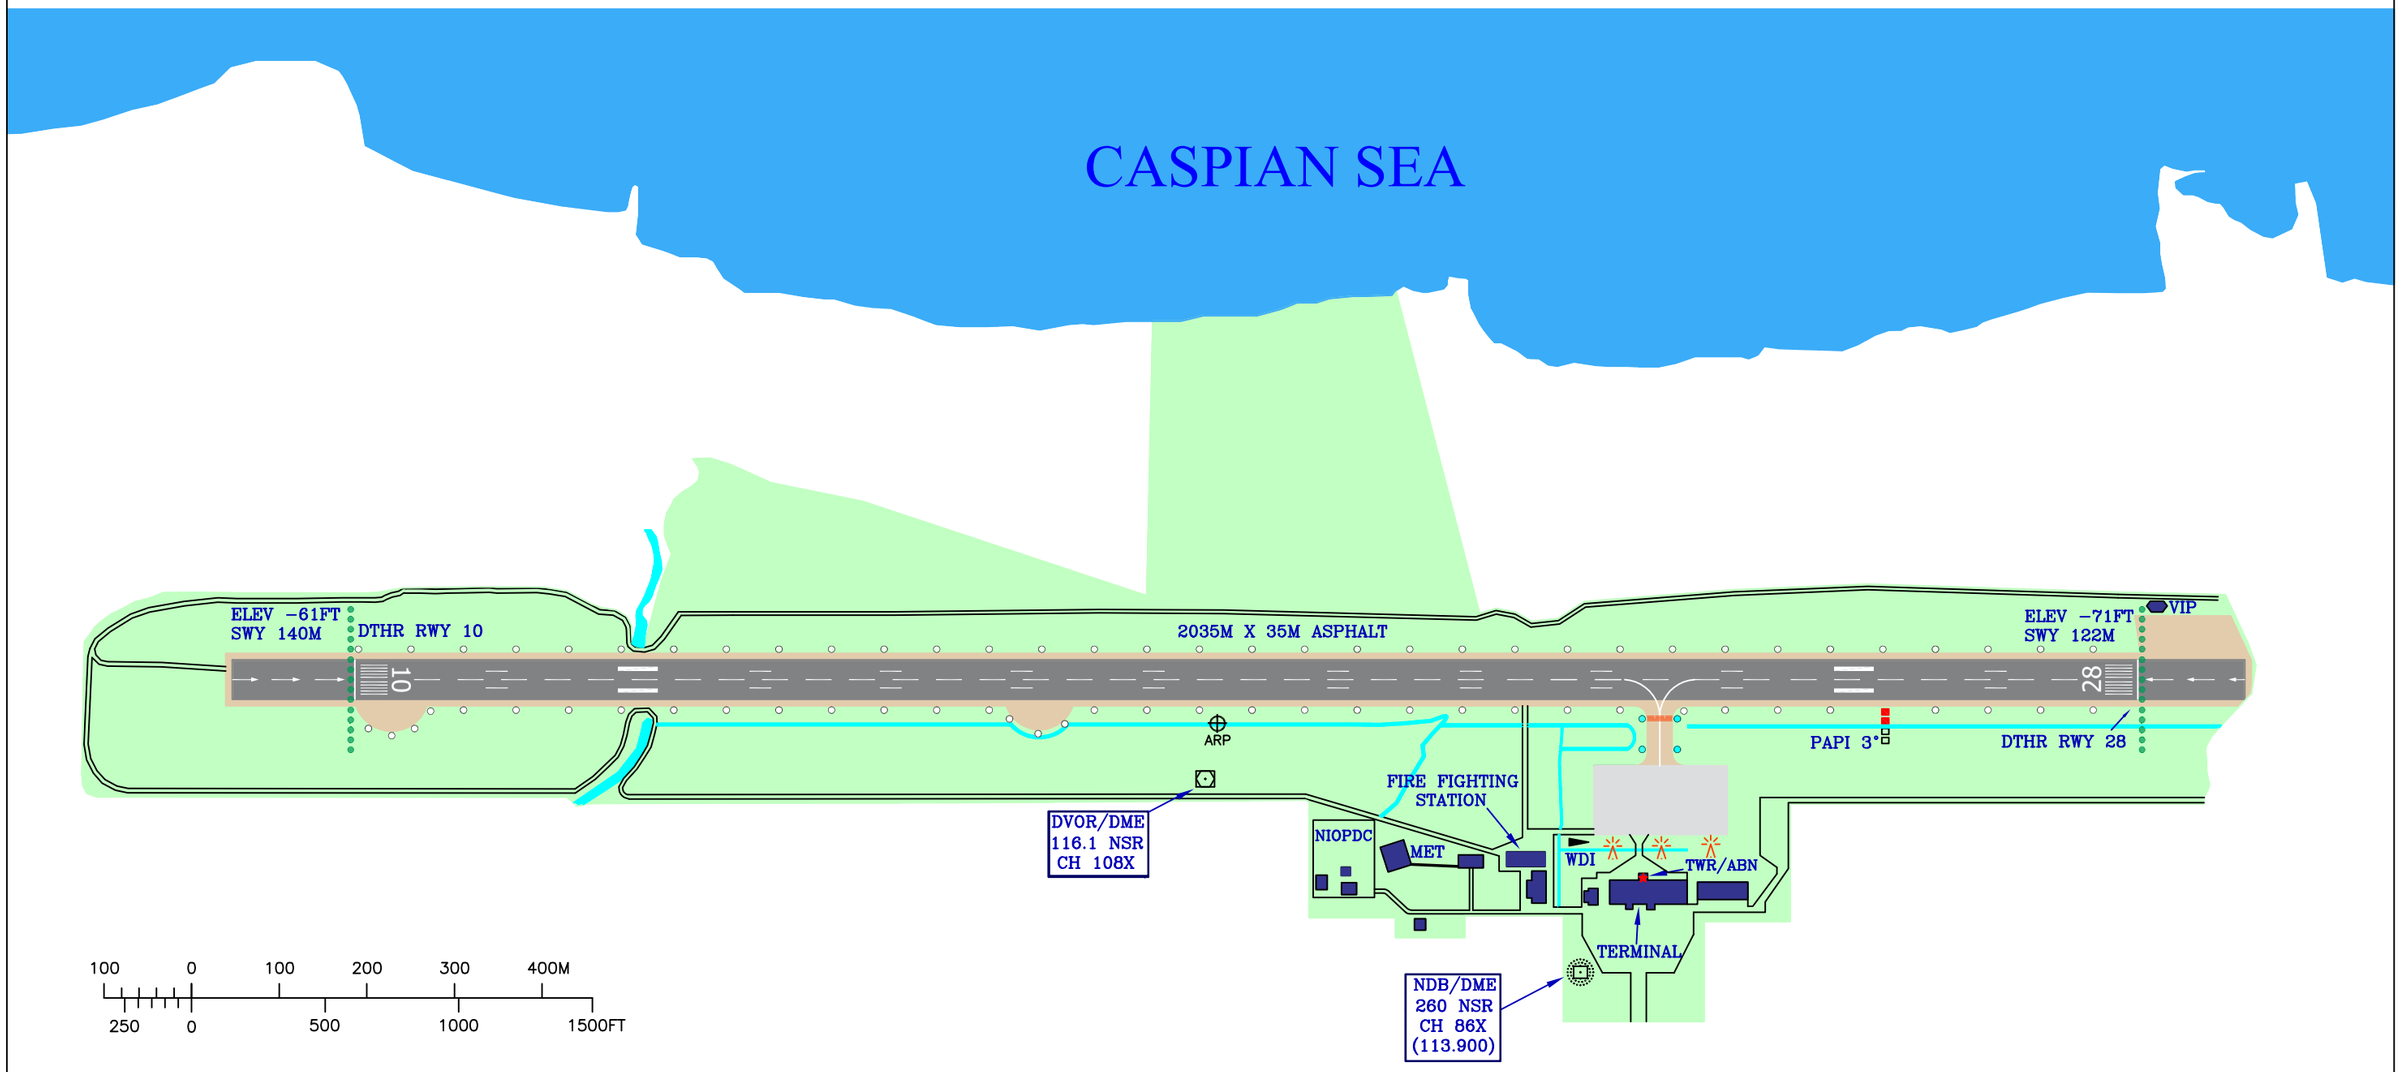

Scale 1:7000