AERODROME CHART - ICAO

ARP 34°20'53" N 047°09'24" E

AD ELEV 4301 FT

TWR 122.450, 121.900
ATIS 126.800

KERMANSHAH/SHAHID ASHRAFI ESFAHANI

RWY	Direction	THR	ELEV	Bearing Strength	GUND
11	116.09°	342106.63N 0470836.17E	4299FT	36/F/C/X/T Asphalt	+26 FT
29	296.09°	342020.75N 0471029.39E	4301FT	36/F/C/X/T Asphalt	+26 FT

PCN RWY Under Construction is 84/F/C/X/T

THR RWY 11 displaced 240M
DTHR COORDINATES: 342103.22N 0470844.61E

All TWY Width are 23M

Apron Surface: Asphalt

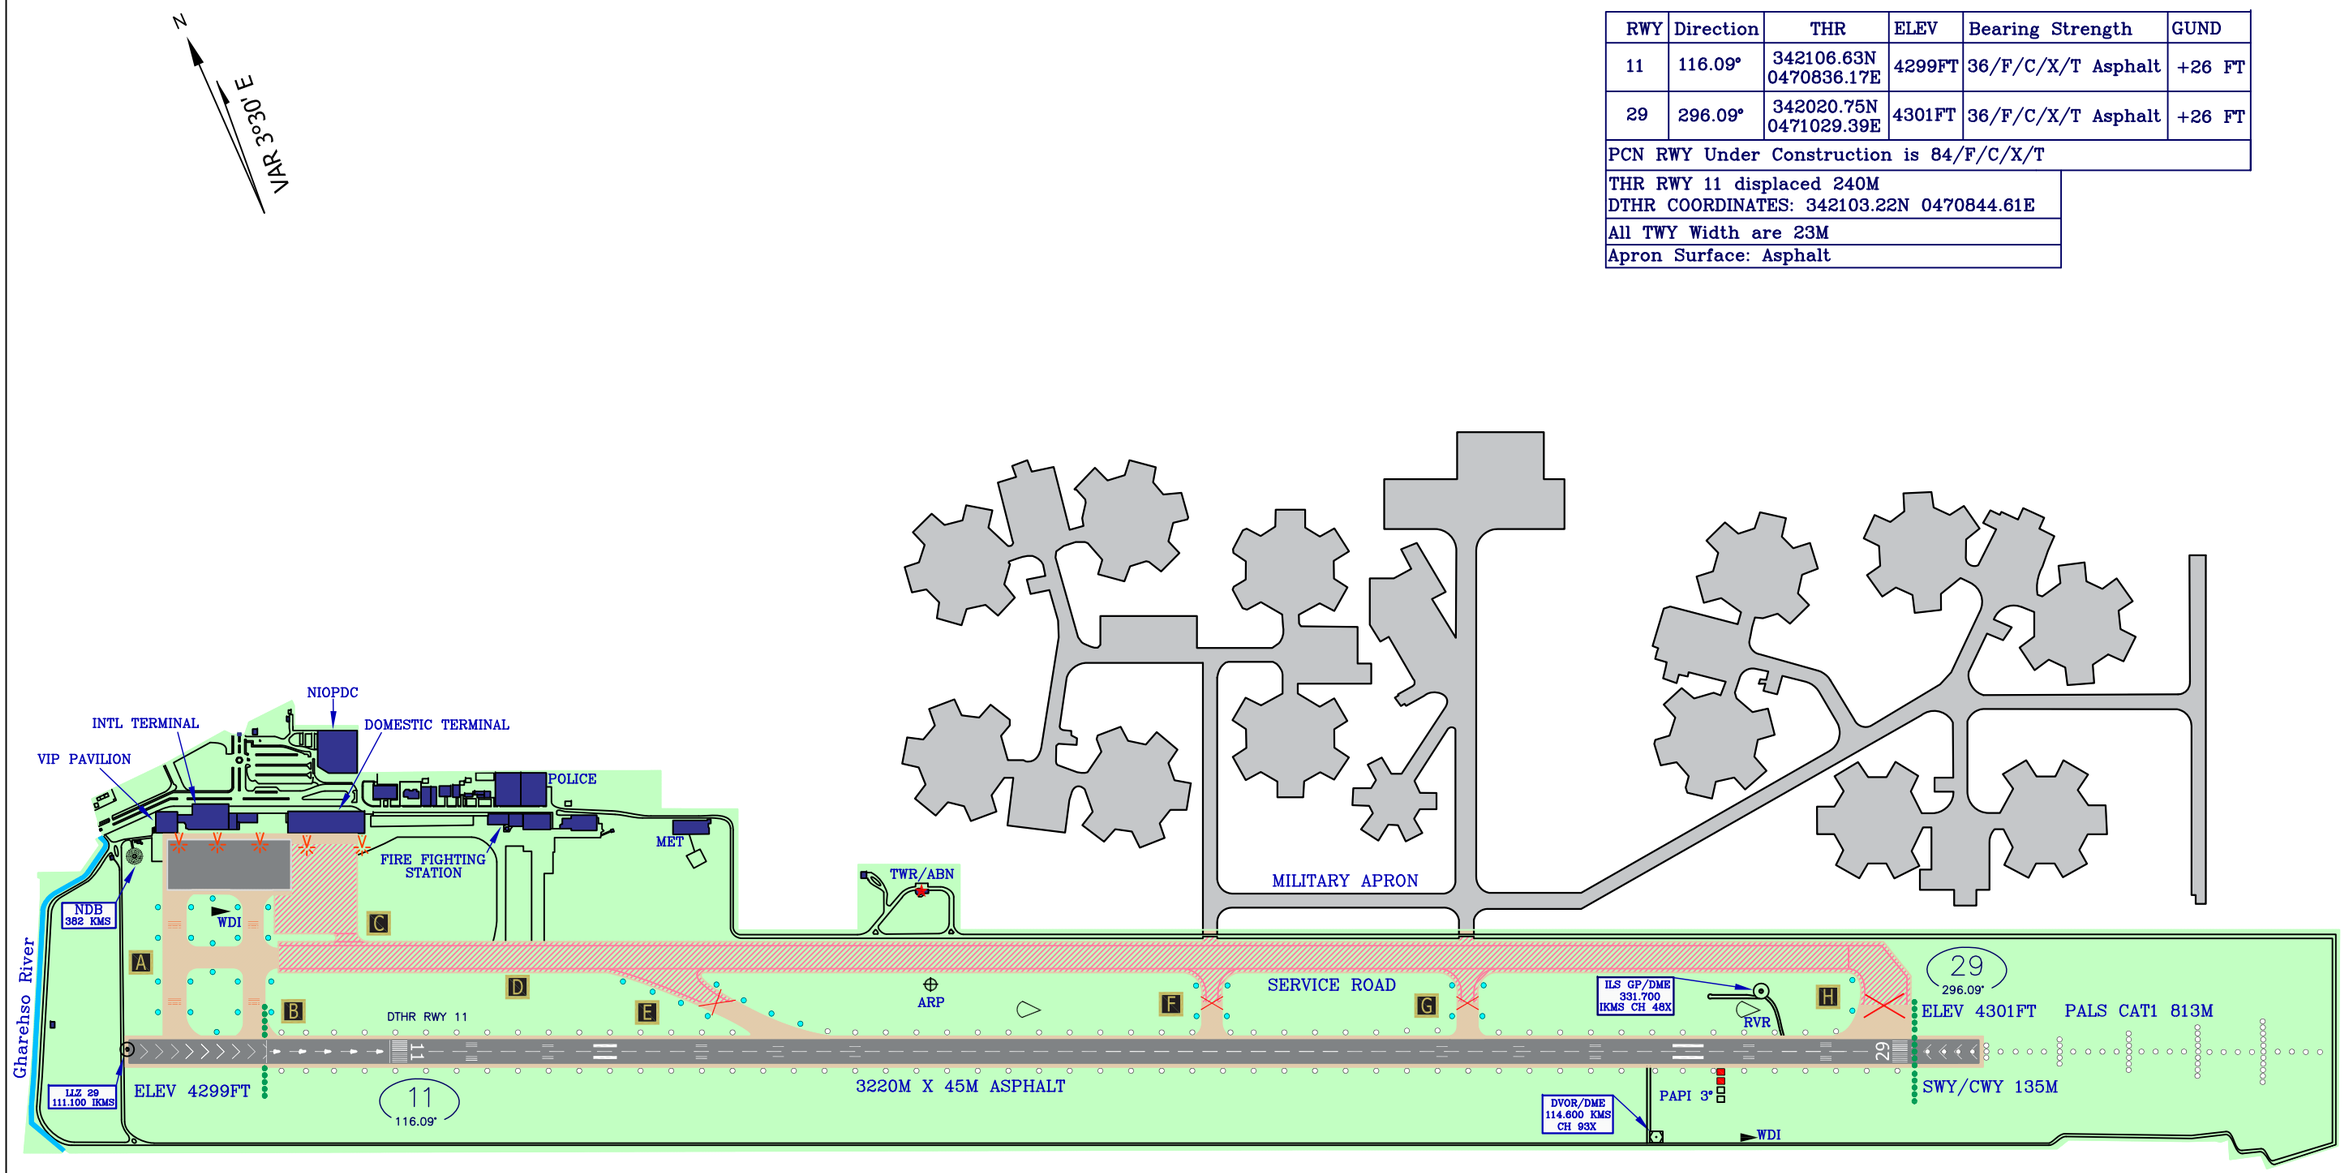

200 0 200 400 600M
500 0 500 1000 1500 2000FT

Scale 1:12000

Building
Concrete
Asphalt
Under Construction