AERODROME CHART - ICAO

ARP 27°13'07" N 056°22'40" E

AD ELEV 22 FT

TWR 118.100	GND 121.900
ATIS 128.650	APP 124.200

BANDAR ABBAS/BANDAR ABBAS INTL

HOT SPOTS

HS 1	Caution unuthorized military vehicles movement.
HS 2	A: Caution fighter aircraft movement. B: Fighters on TWY H must hold short of TWY G.

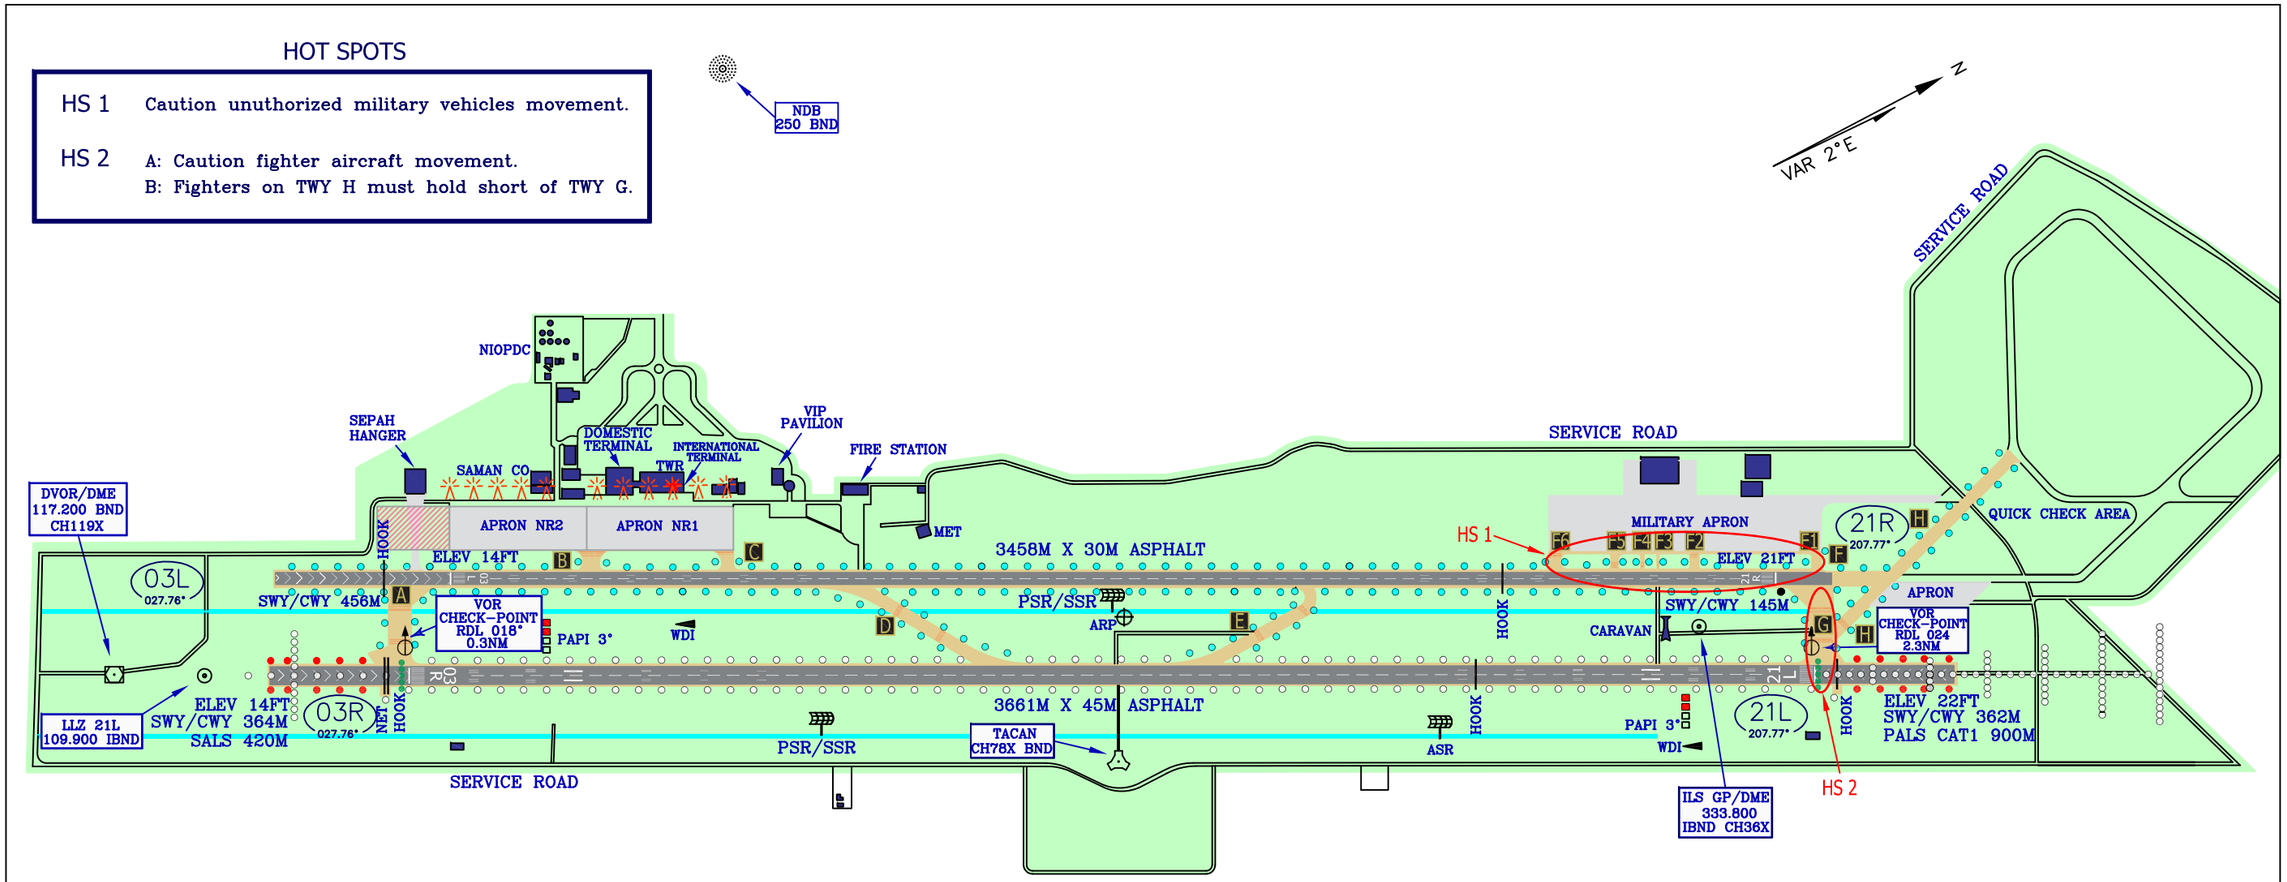

RWY	TRUE BRG	THR	ELEV	Bearing Strength	GUND
03L	027.76°	271218.14N 0562206.97E	14FT	55/F/A/X/T Asphalt	-95 FT
21R	207.77°	271357.55N 0562305.51E	21FT	55/F/A/X/T Asphalt	-95 FT
03R	027.76°	271211.35N 0562213.24E	14FT	65/F/A/X/T Asphalt	-95 FT
21L	207.77°	271356.61N 0562315.21E	22FT	65/F/A/X/T Asphalt	-95 FT

AD Code Letter/Number : 4E

All TWYs width are 30M.

TWY B,C,D and E are Asphalt, PCN:64/F/A/X/T.

TWY A and G are concrete, PCN:60/R/B/W/T.

Apron NR1 Strength: Surface:Asphalt, PCN:65/F/A/X/T

Apron NR2 Strength: Surface:Concrete, PCN:73/R/B/W/U

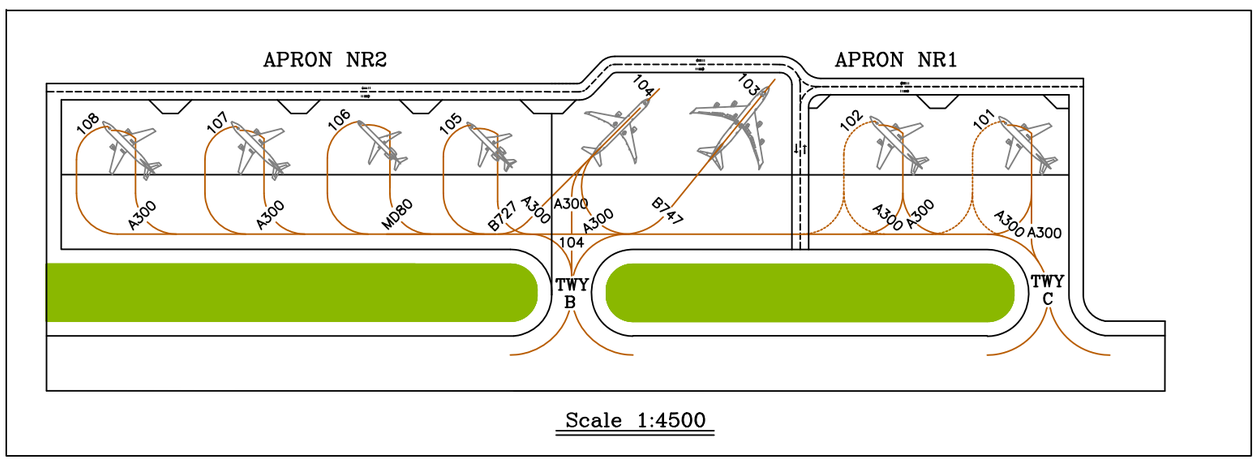

Scale 1:4500

Water canal
Building
Under construction

200M 0 200 400 600M
500FT 0 1000 2000FT

Scale 1:16000