AERODROME CHART - ICAO

ARP 30°16'28" N 056°57'04" E

AD ELEV 5732 FT

TWR 118.250 , 121.900
ATIS 127.250

KERMAN

RWY	Direction	THR	ELEV	Bearing Strength	GUND
16L	158.33°	301721.89N 0565638.79E	5723FT	PCN 50/F/B/X/T	–25 FT
34R	338.34°	301525.67N 0565731.98E	5732FT	PCN 50/F/B/X/T	–25 FT
16R	158.33°	301719.33N 0565631.50E	5723FT	PCN 71/F/C/X/T	–25 FT
34L	338.33°	301523.15N 0565724.67E	5731FT	PCN 71/F/C/X/T	–25 FT

DTHR RWY 34L COORDINATES: 301526.17N 0565723.29E, DTHR 34L: 100M
DTHR ELEVATION: 5731 FT

AD Reference Code: 4D
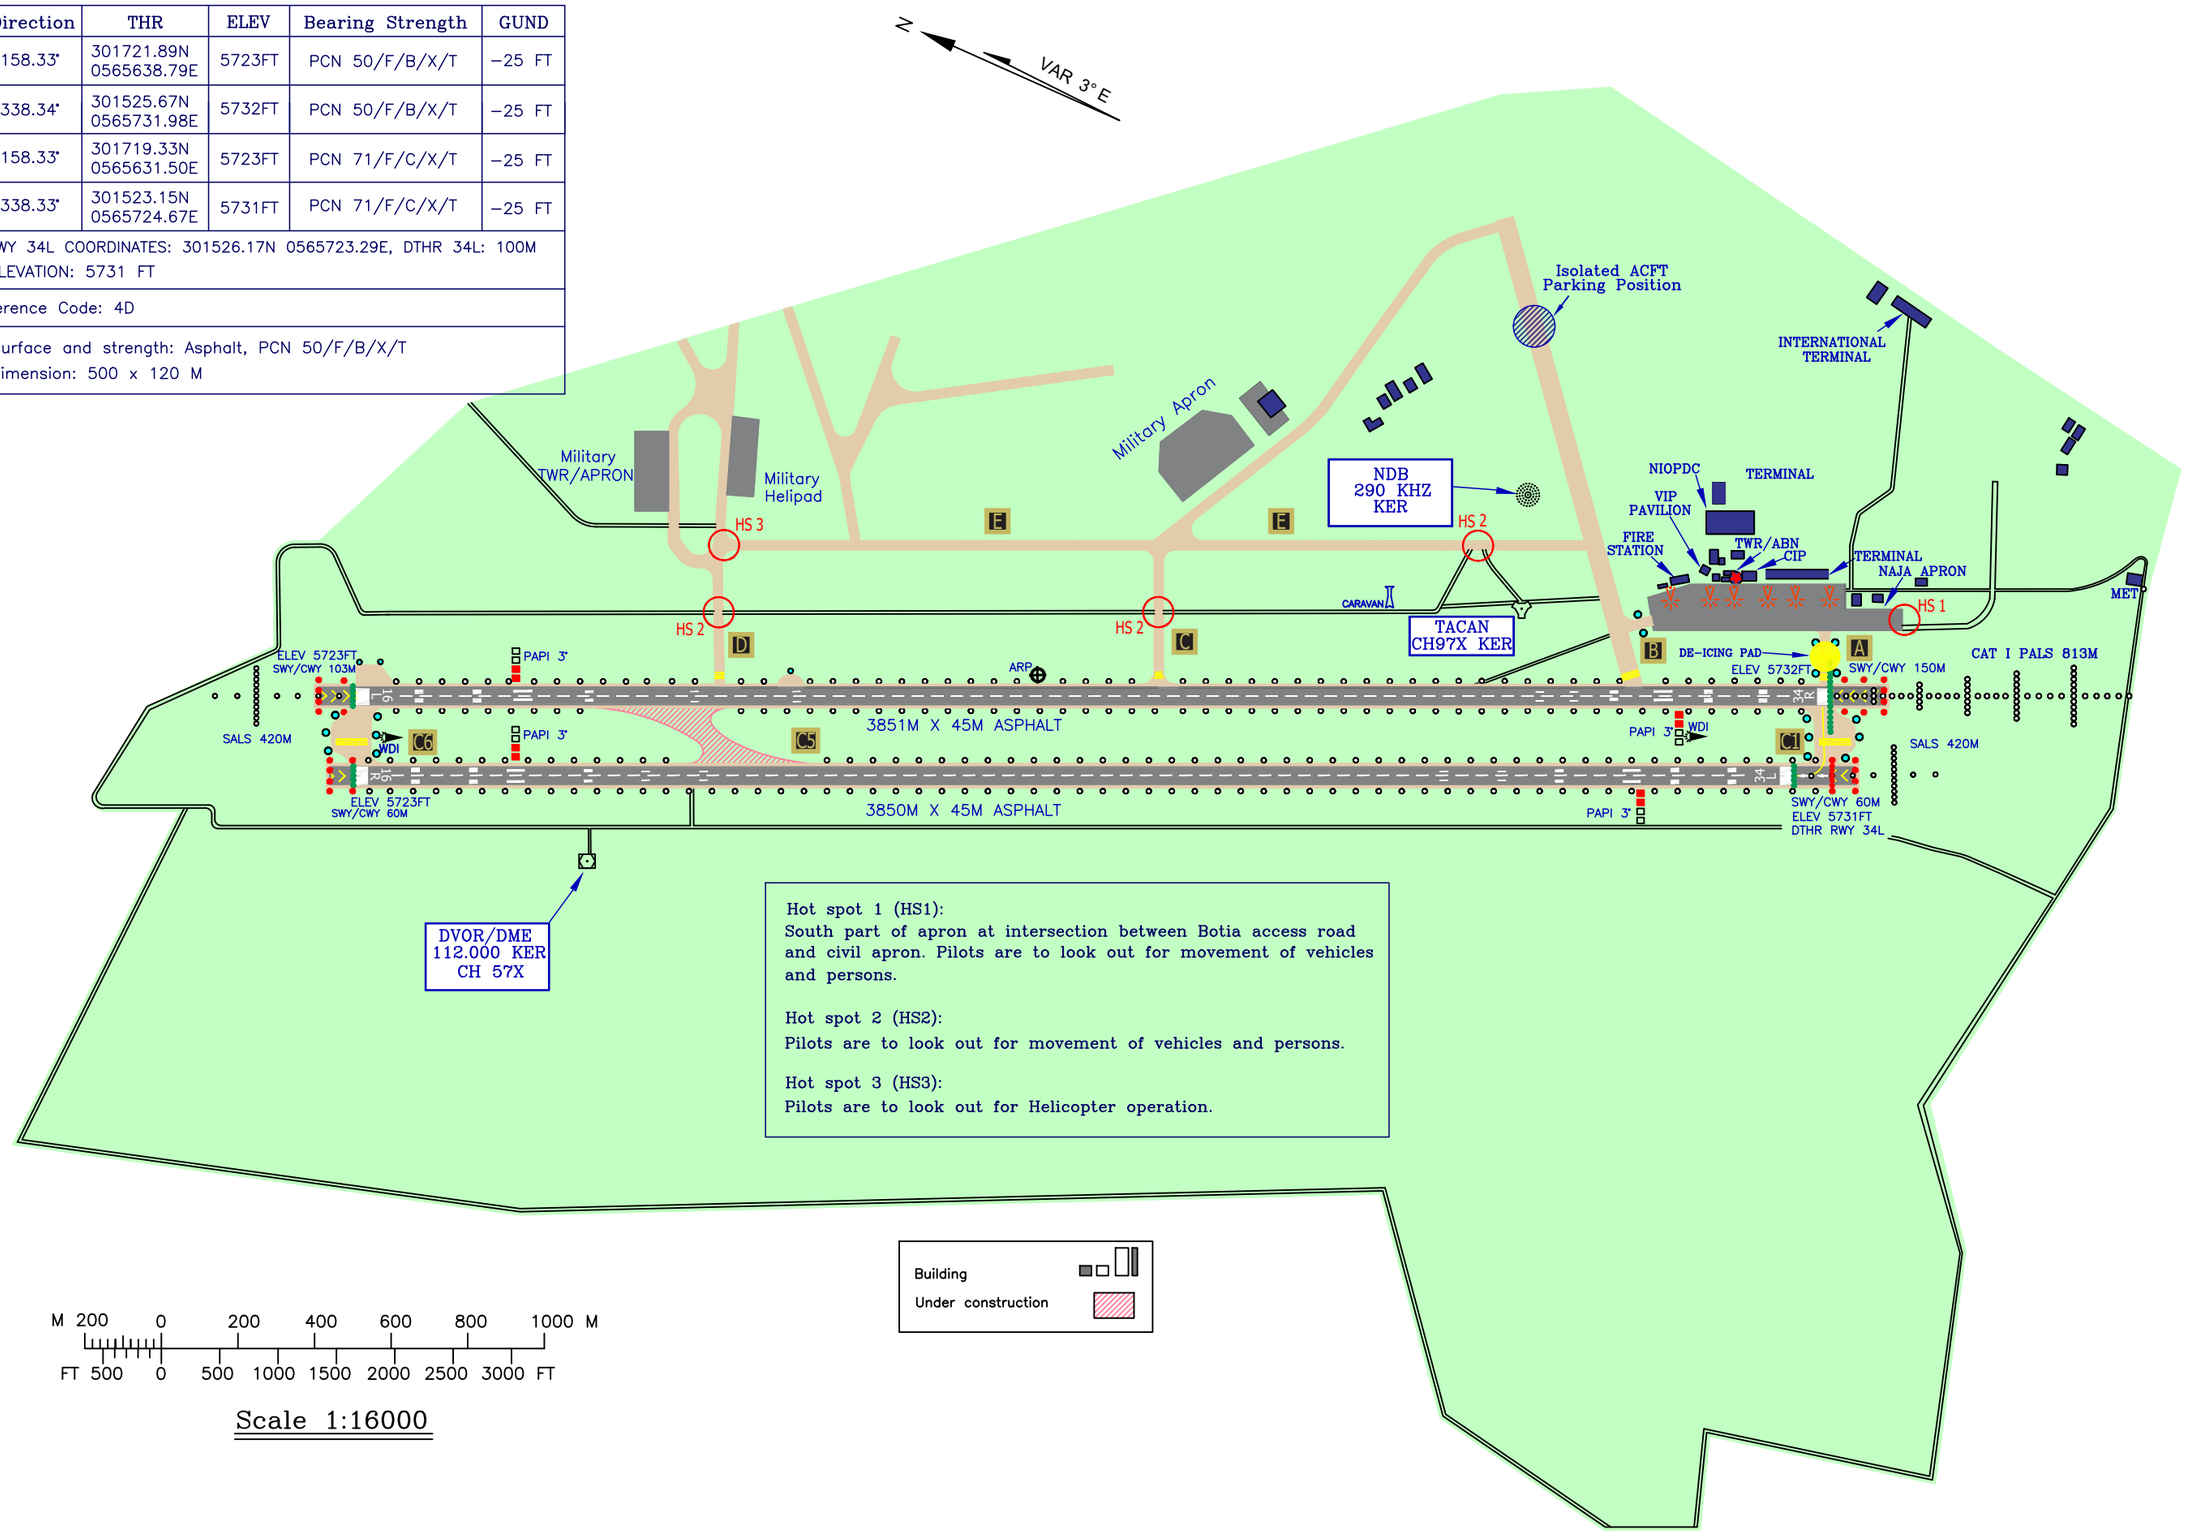
Apron surface and strength: Asphalt, PCN 50/F/B/X/T
Apron dimension: 500 x 120 M