AERODROME CHART - ICAO | ARP 32°45'03" N 051°51'46" E | AD ELEV 5058 FT | TWR 118.300 GND 121.900 ATIS 128.250 | ESFAHAN/SHAHID BEHESHTI INTL

N
VAR 4°E

HOT SPOT:
HS 1 : AIRCRAFT AND VEHICLES USING TWY A TO LEAVE THE APRON, MUST HOLD SHORT OF RWY 25L/07R.
HS 2 : AIRCRAFT AND VEHICLES USING TWY B TO LEAVE THE APRON, MUST HOLD SHORT OF RWY 25L/07R.
HS 3 : AIRCRAFT AND VEHICLES USING TWY C TO LEAVE THE APRON, MUST HOLD SHORT OF RWY 25L/07R.
HS 4 : AIRCRAFT AND VEHICLES USING TWY G, MUST HOLD SHORT OF RWY 25R/07L.
HS 5 : AIRCRAFT AND VEHICLES USING TWY M, MUST HOLD SHORT OF RWY 25R/07L.

RWY	Direction	THR	ELEV	Bearing Strength	GUND
07L	077.93°	324455.45N 0515016.15E	5056.7FT	65/F/C/X/T Asphalt	0
25R	257.96°	324525.27N 0515301.41E	5043.4FT	65/F/C/X/T Asphalt	0
07R	077.93°	324440.85N 0515019.84	5058.1FT	65/F/C/X/T Asphalt	0
25L	257.96°	324510.67N 0515305.08E	5037.1FT	65/F/C/X/T Asphalt	0

All TWY 23M, TWY S 7M, TWY G and J 85M.
The first 305M of each RWY is concrete.
APRON PCN : 75/R/B/W/T Concrete

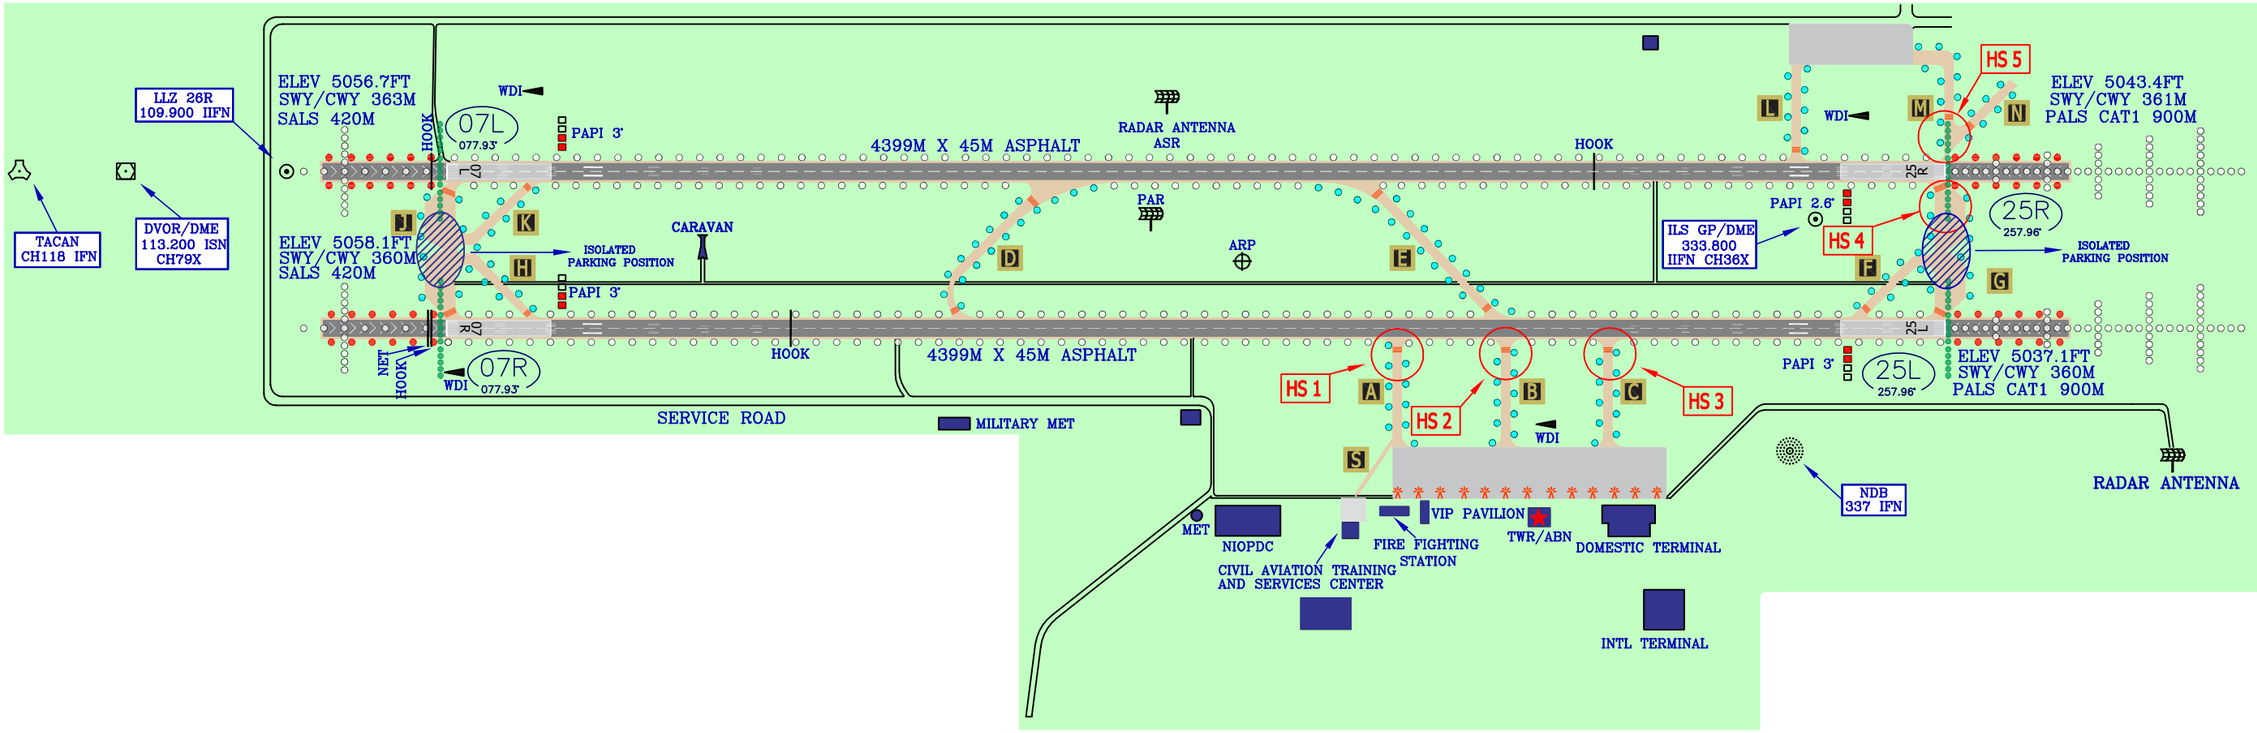

Building
Concrete
Asphalt

200M 0 200 400 600M
500FT 0 1000 2000FT

Scale 1:18000