AERODROME CHART - ICAO

Shiraz/Shahid Dastghaib INTL

Scale 1 : 18000

200M 0 400 800M

500FT 0 1000 2000FT

N VAR 3°E

Hotspot 1: After landing at 29L/11R hold short of RWY 29R/11L and look out for departing aircraft

Hotspot 2: Taxiing aircraft look out for landing and departing aicraft on RWY 29L/11R

Aerodrome Elevation : 4917 FT

Aerodrome Lighting			
RWY 11L	RWY 29R	RWY 11R	RWY 29L
SALS THRL REDL RENL WBL SWYL	PALS PAPI THRL REDL RENL WBL SWYL	SALS THRL REDL RENL WBL SWYL	PALS PAPI THRL REDL RENL WBL SWYL

ABN : FLG Green, White

Apron : INFO not AVBL

TWY Lighting

Edge : TWYs A, A1 to A5, A7, B1, B2, B4, B5, B7, G3 and G

Center Line : NIL

ATS Communication Facilities	
Service Designation	Frequency
TWR	118.100
GND	121.900, 121.750
ATIS	127.000 Z
AFIS (Information)	--

AD Reference Code : 4E

Displaced Threshold

NIL

RWY	Direction	Elevation	THR Coordinates	GUND	Bearing Strength (PCN) and Surface
11L	114.45°	4912 FT	293256.90N 0523413.61E	-31 FT	85/F/C/W/T Asphalt
29R	294.47°	4864 FT	293158.61N 0523640.12E	-31 FT	85/F/C/W/T Asphalt
11R	114.46°	4917 FT	293242.53N 0523408.72E	-31 FT	80/F/C/W/T Asphalt
29L	294.48°	4860 FT	293145.09N 0523633.08E	-31 FT	80/F/C/W/T Asphalt

VOR check point	Coordinates: 293152.1N 0523638.0E , Radial: 113° , Distance: 1.3 NM .

TWY	Width : All TWYs 23M except: TWY A2: 29M; TWYs A3, A4, A5, G3, G4: 26M Surface : Asphalt Strength (PCN) : INFO not AVBL
Apron	Surface : Concrete Strength (PCN) : INFO not AVBL Dimensions : 930 x 100 M
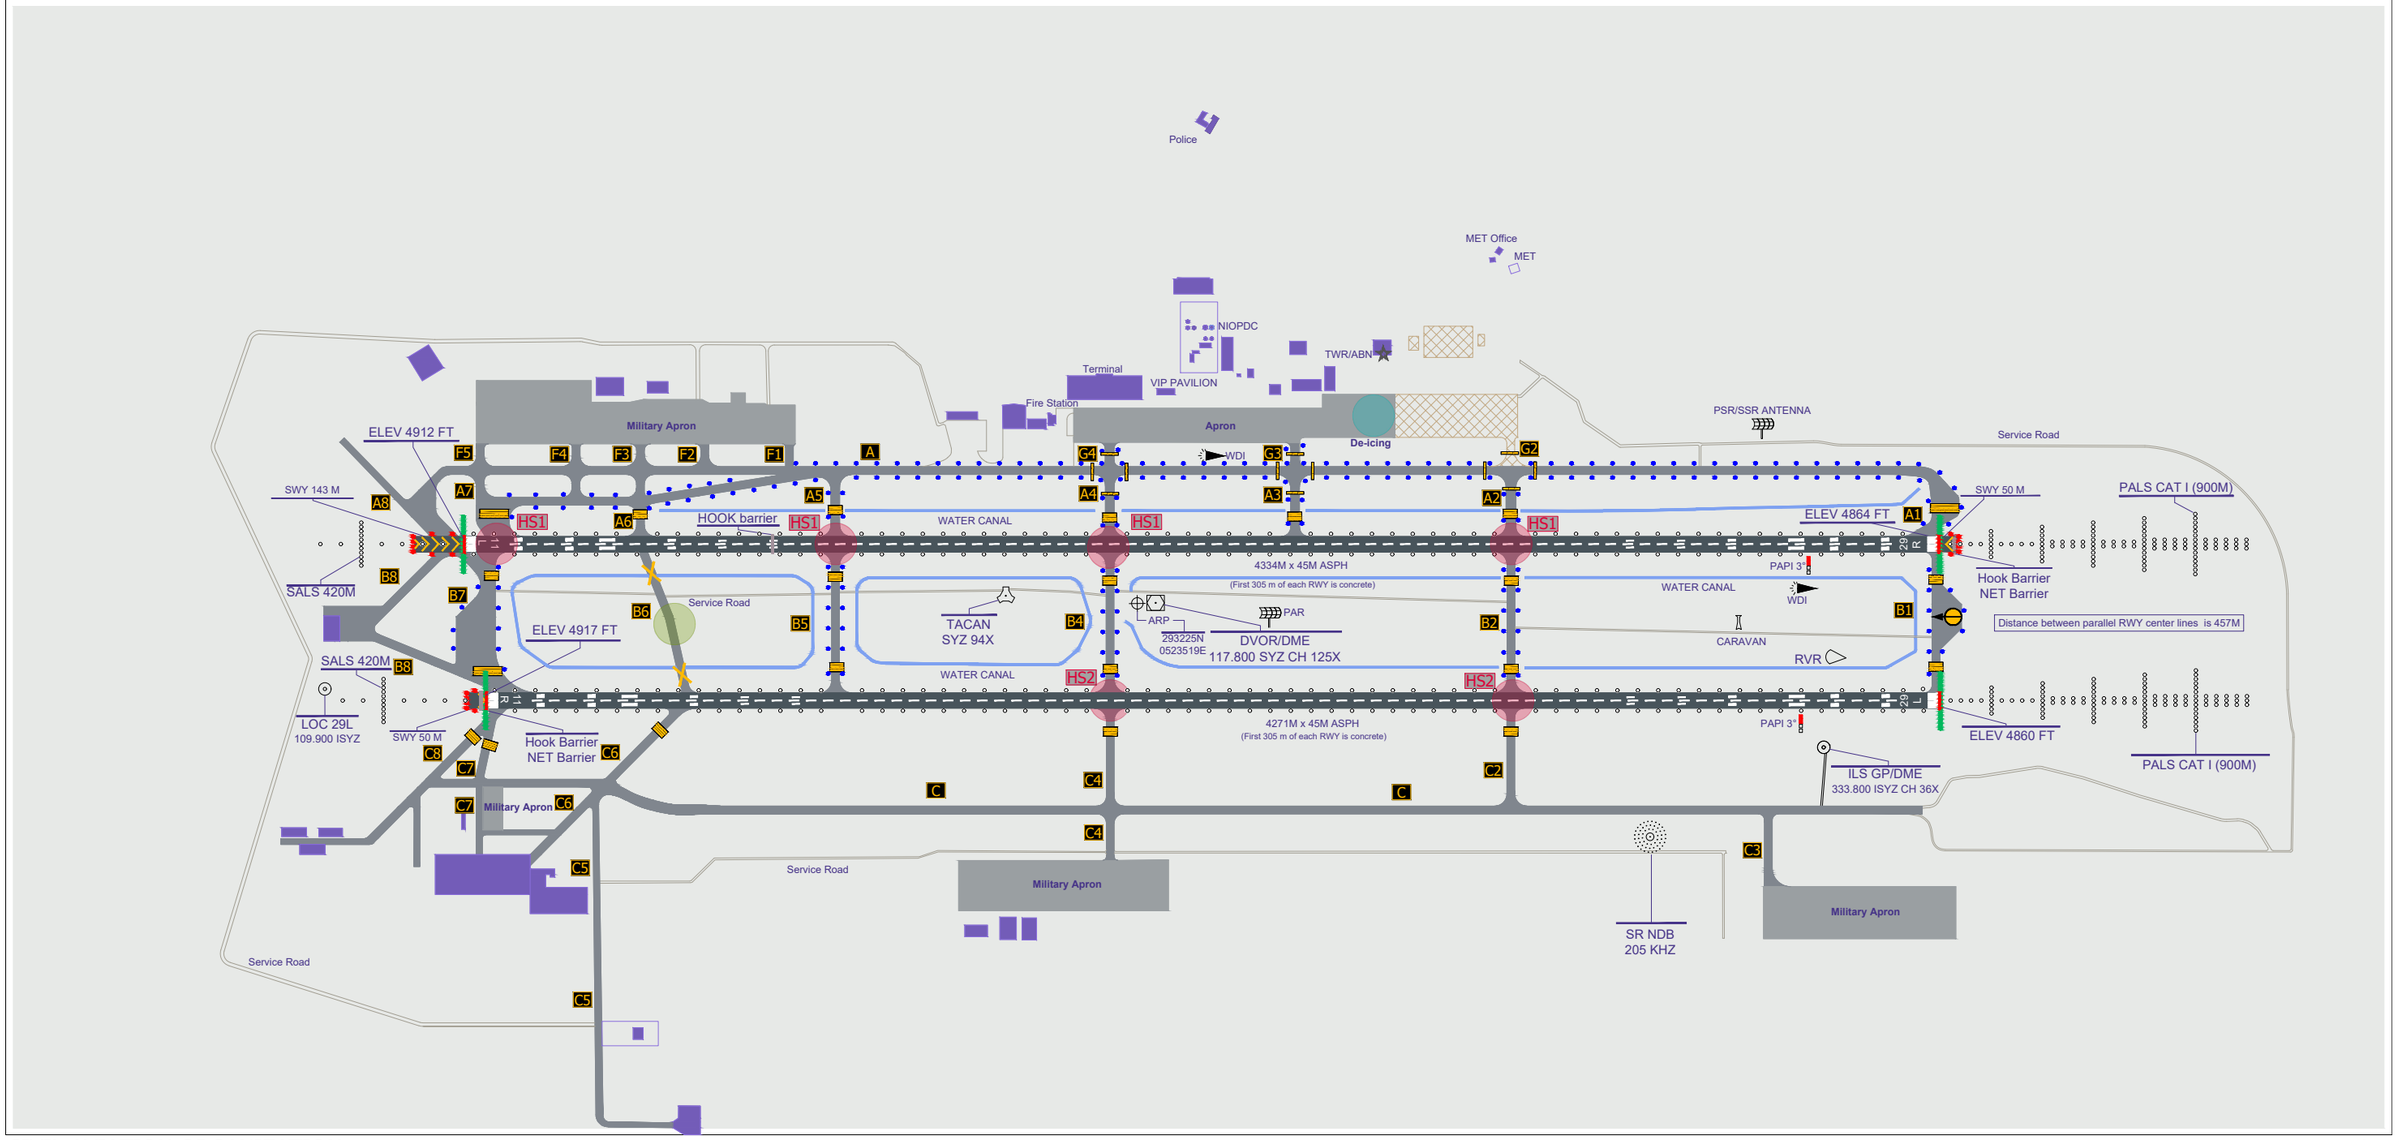
Apron
Taxiway
Runway
Building
Hotspot
Isolated ACFT Parking Position
Deicing Pad
Under Construction