AERODROME CHART - ICAO

ARP 37°40'17" N
045°04'09" E

AD ELEV 4342 FT

TWR 118.250, 121.900
ATIS 127.250

UROMIYEH

RWY	Direction	THR	ELEV	Bearing Strength	GUND
03	033.02°	373921.03N 0450331.21E	4342FT	58/F/C/X/T Asphalt	+65 FT
21	213.04°	374049.45N 0450443.55E	4274FT	58/F/C/X/T Asphalt	+65 FT

Taxiway width, surface and strength:
Width: 23M
Surface: Asphalt
Strength: Information not available

Apron Surface: Asphalt, Strength: Information not available
Apron dimension: 520M X 152M

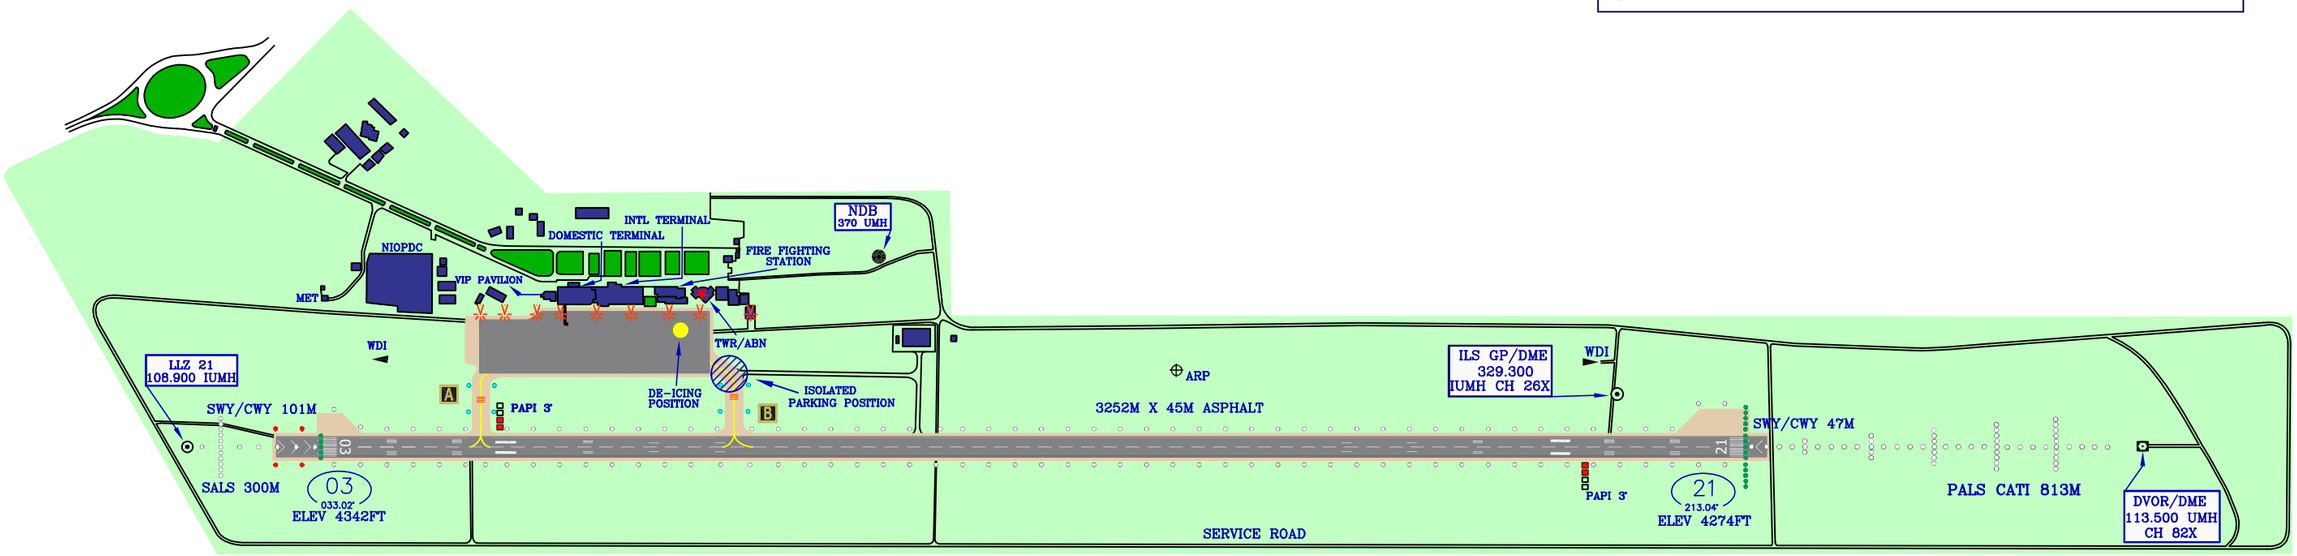

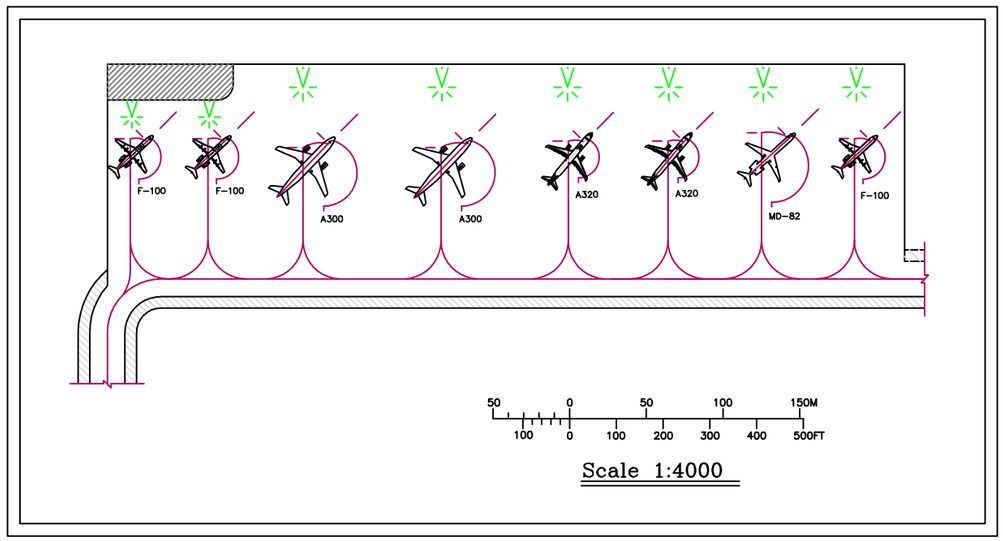

Scale 1:4000

Building
Concrete
Asphalt

200 0 200 400 600M
500 0 500 1000 1500 2000FT

Scale 1:14000