AD Elevation : 5380 FT

Scale 1:11000

200M 0 200 400 600M
500FT 0 500 1000 1500 2000FT

N
VAR 5°E

Hotspot : NIL

Aerodrome Lighting	
RWY Lighting	
12	30
PAPI THRL RENL REDL SWYL WBL	SALS PAPI THRL RENL REDL SWYL WBL

Other Lighting

ABN : FLG Green, White
TWY Edge : TWY A Blue
Apron : Edge Lg Blue

COM		
TWR	GND	AFIS (Information) 122.950 121.750
-	-	

Hotspot	Isolated ACFT Parking Position	Under Construction	Building
Runway	Taxiway	Apron	Deicing Pad

RWY	Direction	Elevation	THR	GUND	Bearing Strength
12	126.51°	5308 FT	364657.94N 0482038.80E	+37 FT	50/F/B/X/T Asphalt
30	306.52	5380 FT	364556.19N 0482222.51E	+37 FT	50/F/B/X/T Asphalt
-	-	-	-	-	-
-	-	-	-	-	-

AD Reference Code : 4C
Displaced Threshold
NIL
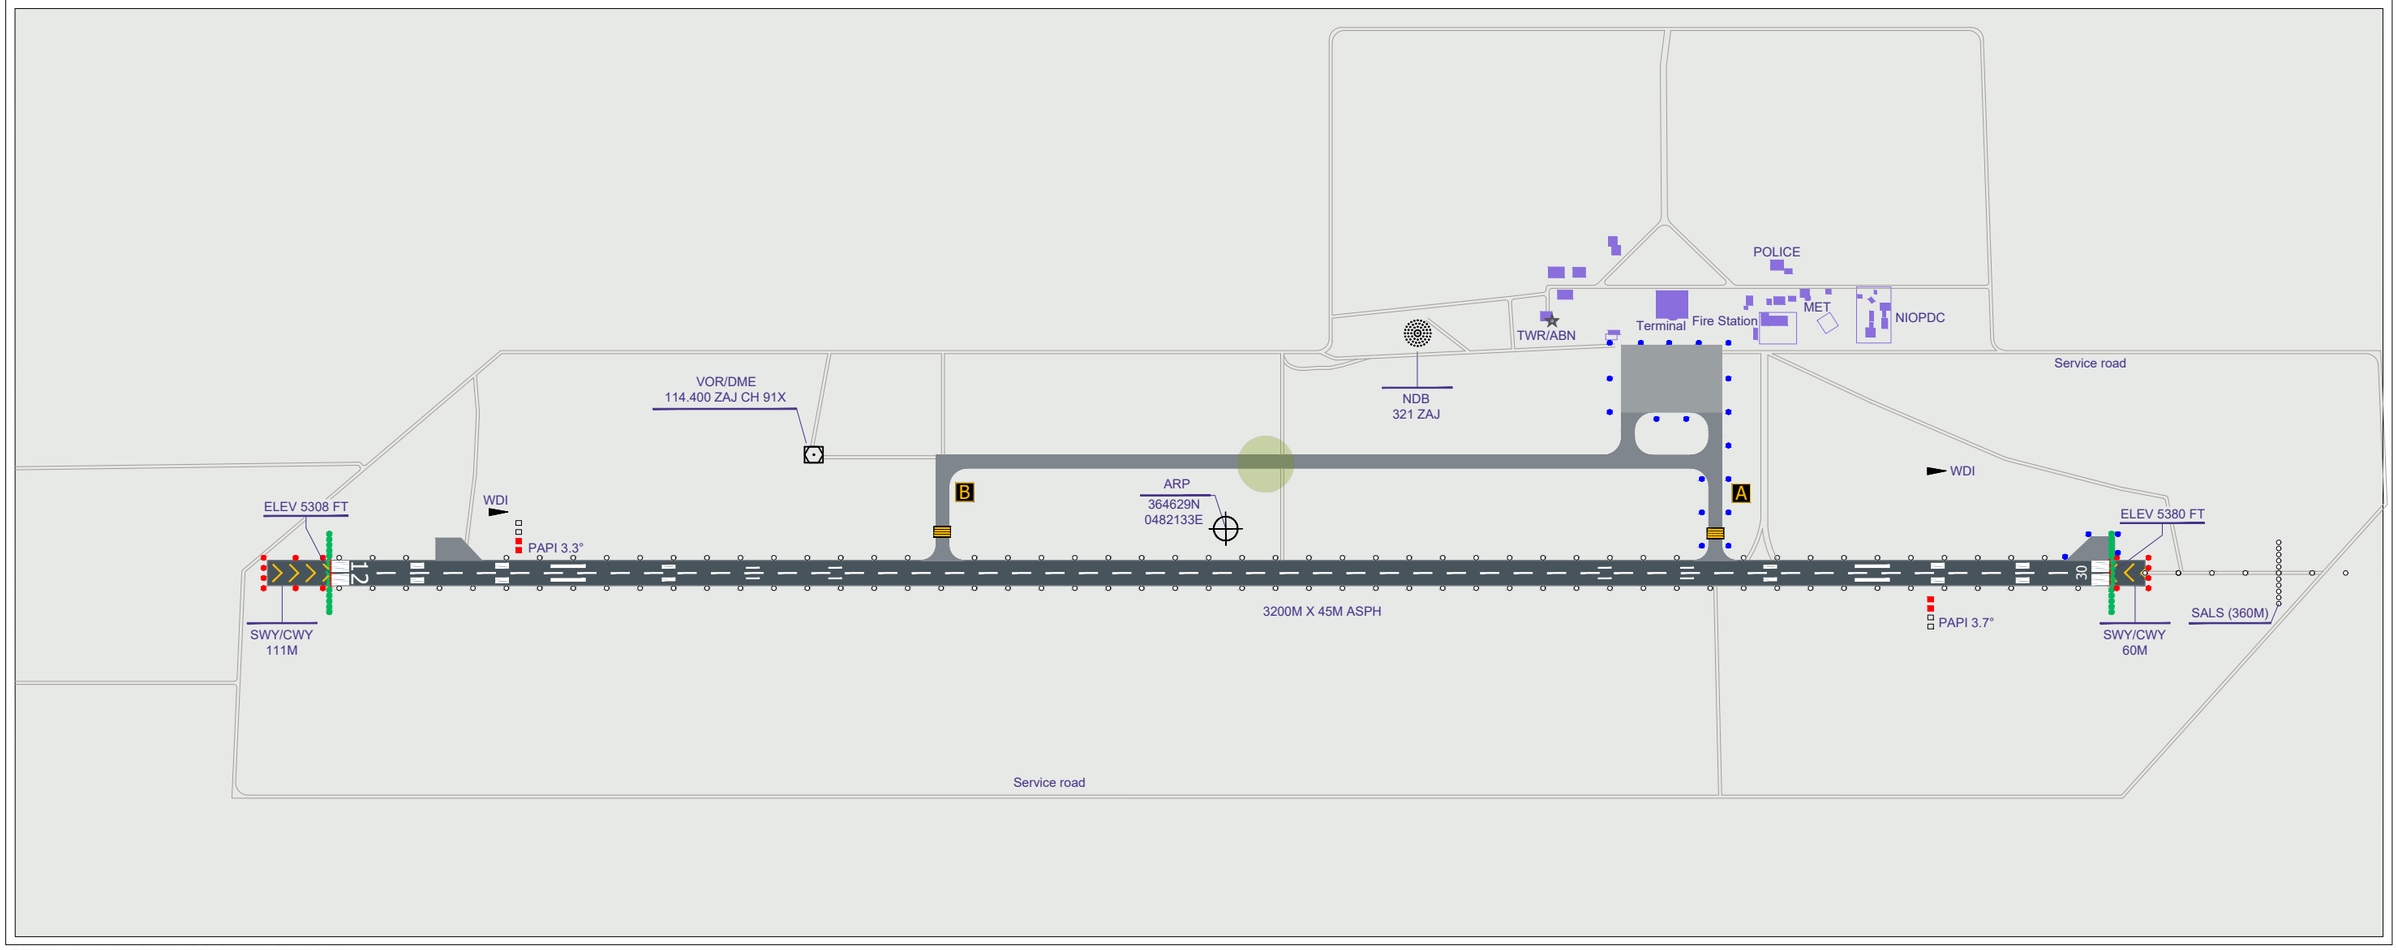
TWY	Width : 23M Surface : Asphalt Strength : INFO not AVBL
Apron	Surface : Asphalt Strength : INFO not AVBL Dimensions : 120M x 200M
Location of VOR check point	NIL